
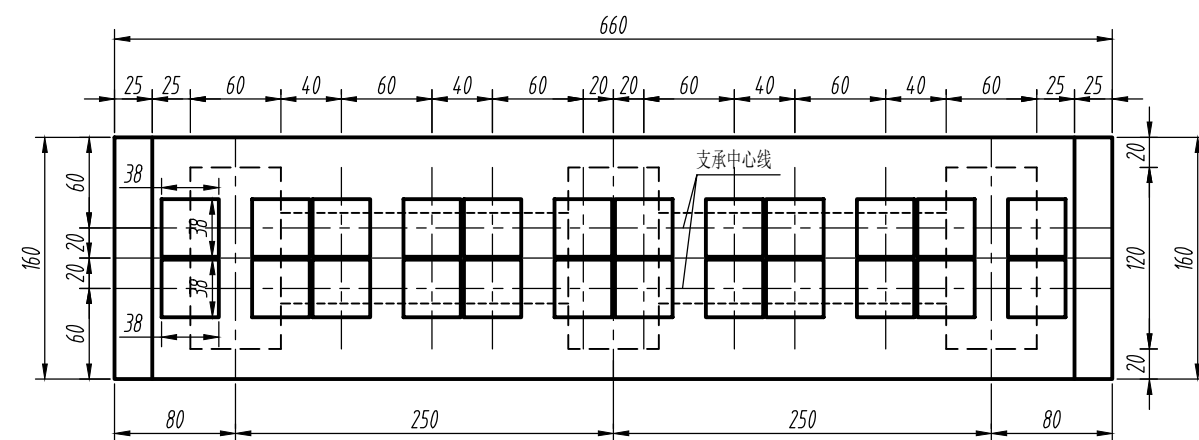


拱桥立柱及盖梁立面图 1:50

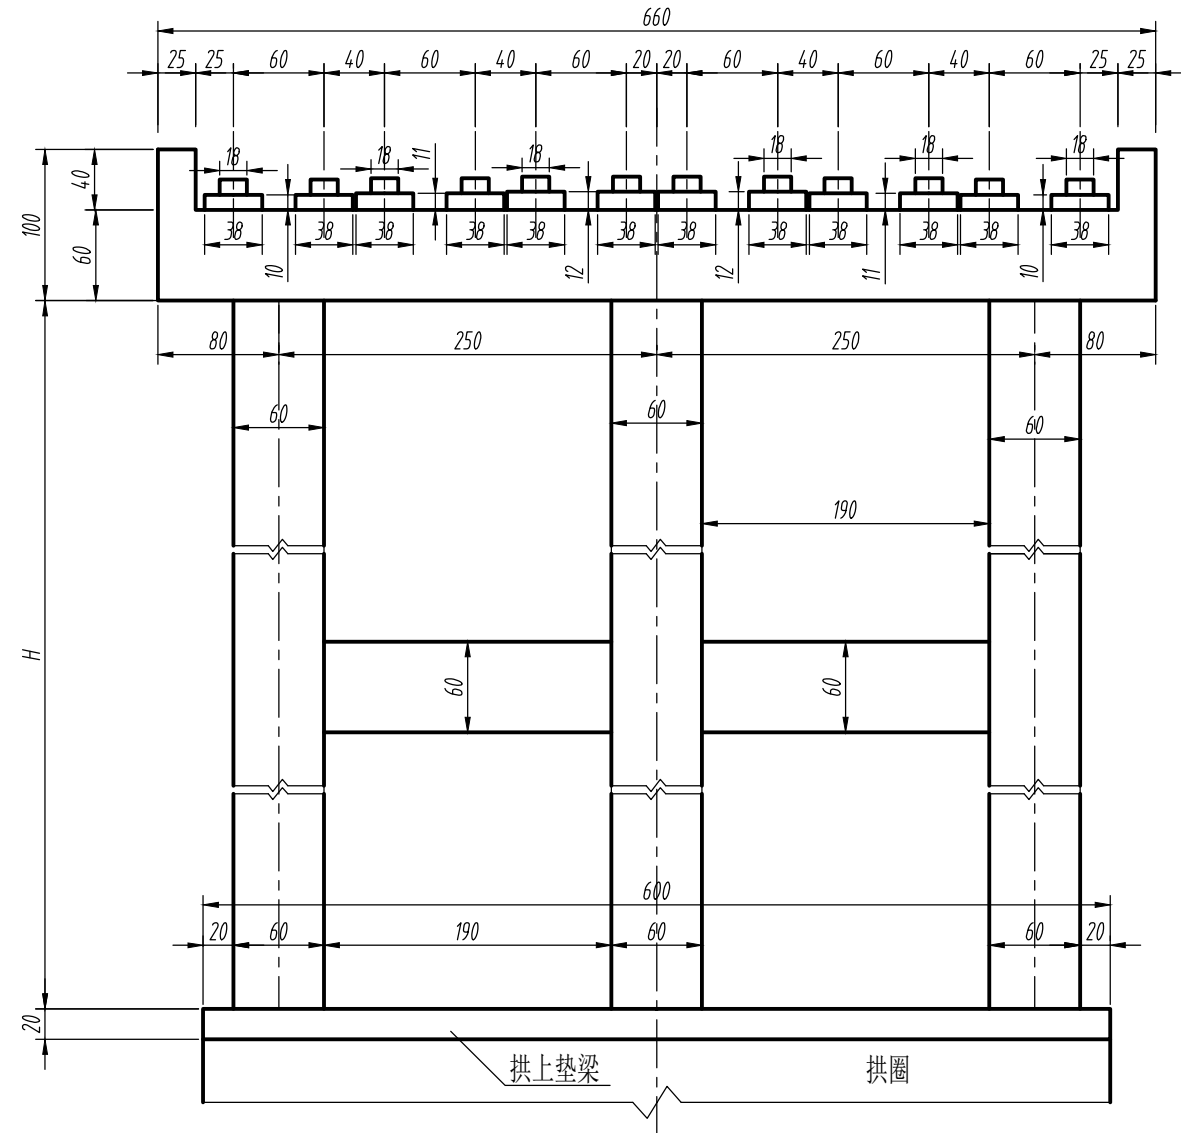


附注:

- 1、本图尺寸除高程、里程桩号以米计外，其余均以厘米为单位。
- 2、拱上立柱编号详见《桥型布置图1》。
- 3、本图适用于1#、2#、9#、10#拱上立柱，本图中立柱尺寸H，以及垫梁尺寸a、b，系梁高度M取值如下表所示。
- | 拱上立柱编号 | 1#立柱 | 2#立柱 | 9# |
|--------|------|------|----|
|--------|------|------|----|

平面图 1:50

拱上立柱编号	1#立柱	2#立柱	9#立柱	10#立柱
拱上垫梁尺寸a	66.1	54.1	54.1	66.1
拱上垫梁尺寸b	113.5	89.1	89.1	113.5
拱上立柱高度H	1283.5	789.1	950.1	1490.5
拱上立柱系梁M	641.75	394.55	475.05	745.25

侧面图 1:50

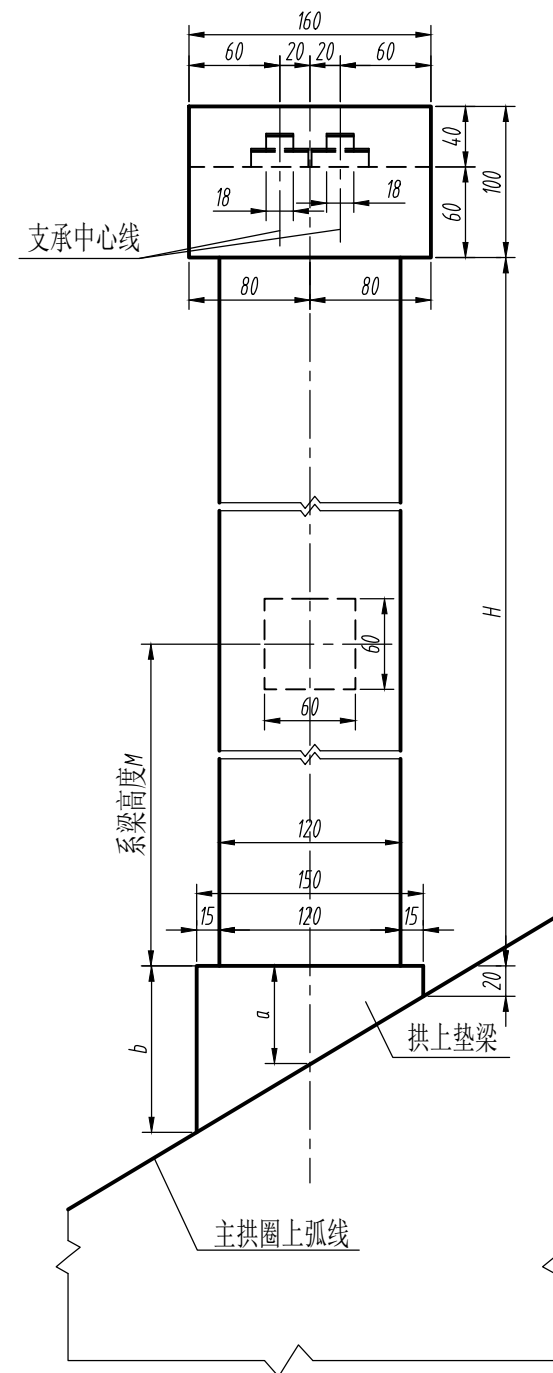

竞赛名称	第十七届"高教杯"全国大学生先进成图技术与产品信息建模创新大赛(道桥类)			
图名	拱上立柱及盖梁构造图1			
图号	DQ-5	总分	200分	时间 180分钟