





第15页 共18页

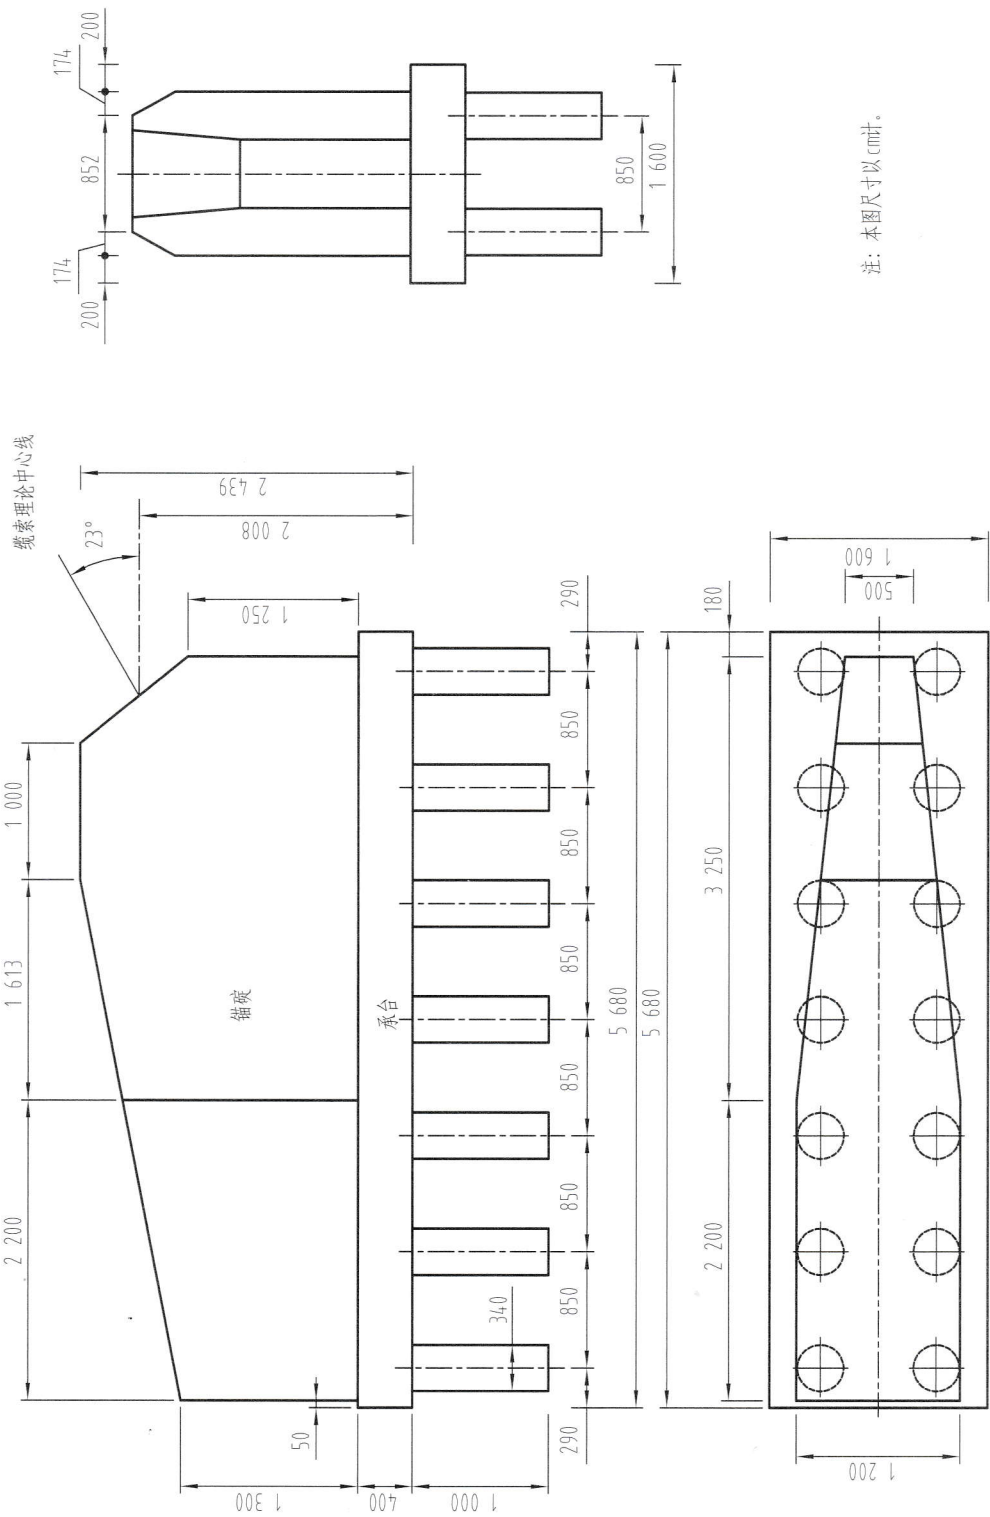

注: 本图尺寸以 cm 计。

图名	比例	图号
索锚结构构造图		JS-12

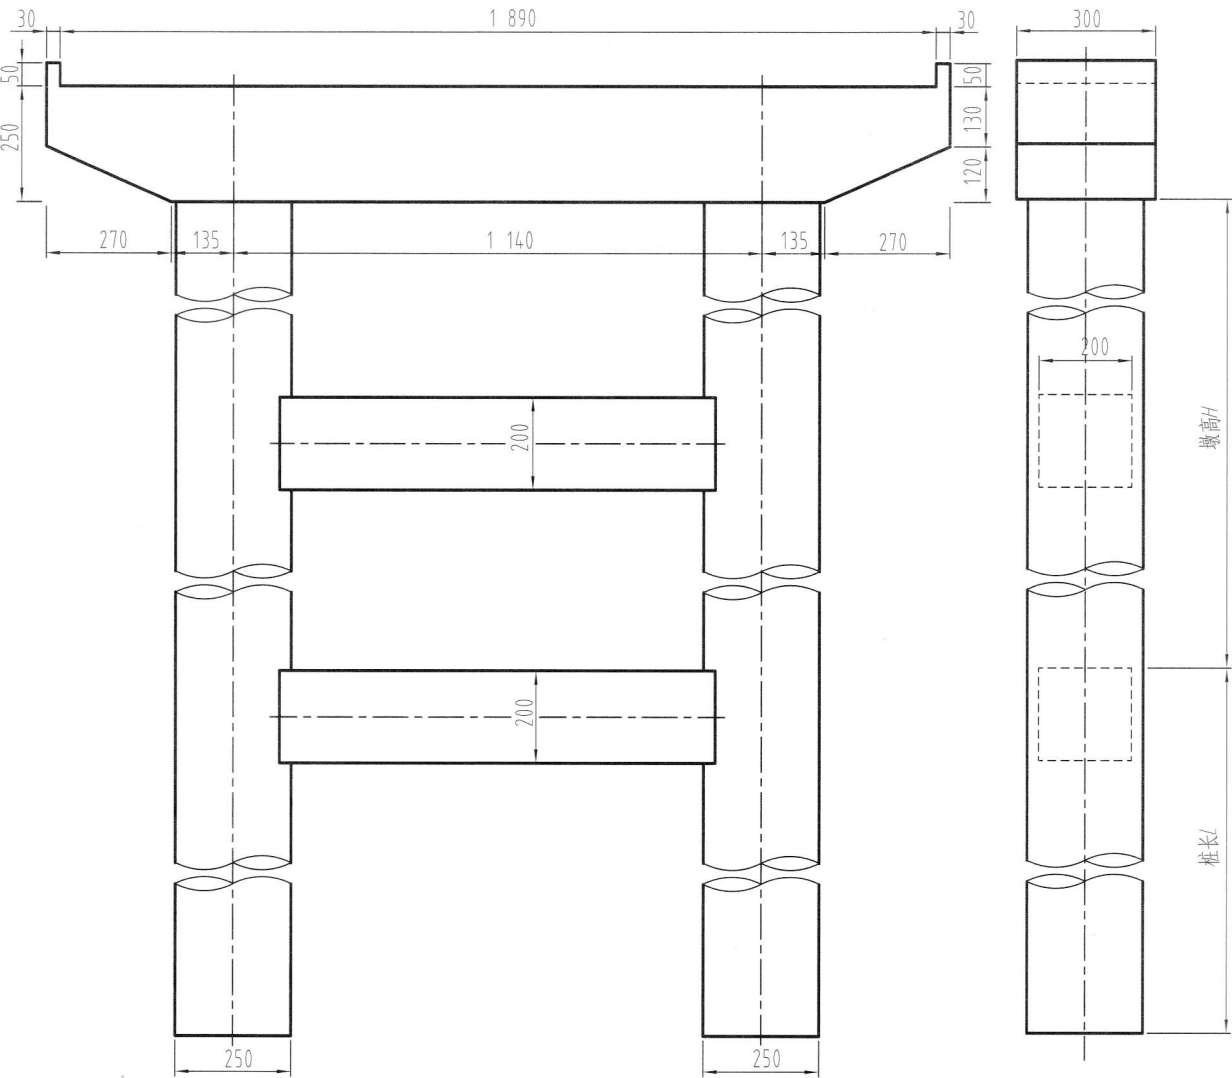

注：本图尺寸以 cm 计。

图名	引桥桥墩构造图	比例	
		图号	JS-14